

GAMBAR PERENCANAAN


NAMA PEKERJAAN

PERENCANAAN BANGUNAN RUKO


LOKASI

PERENCANAAN BANGUNAN RUKO
SOPIAN SORI

TAHUN
2025

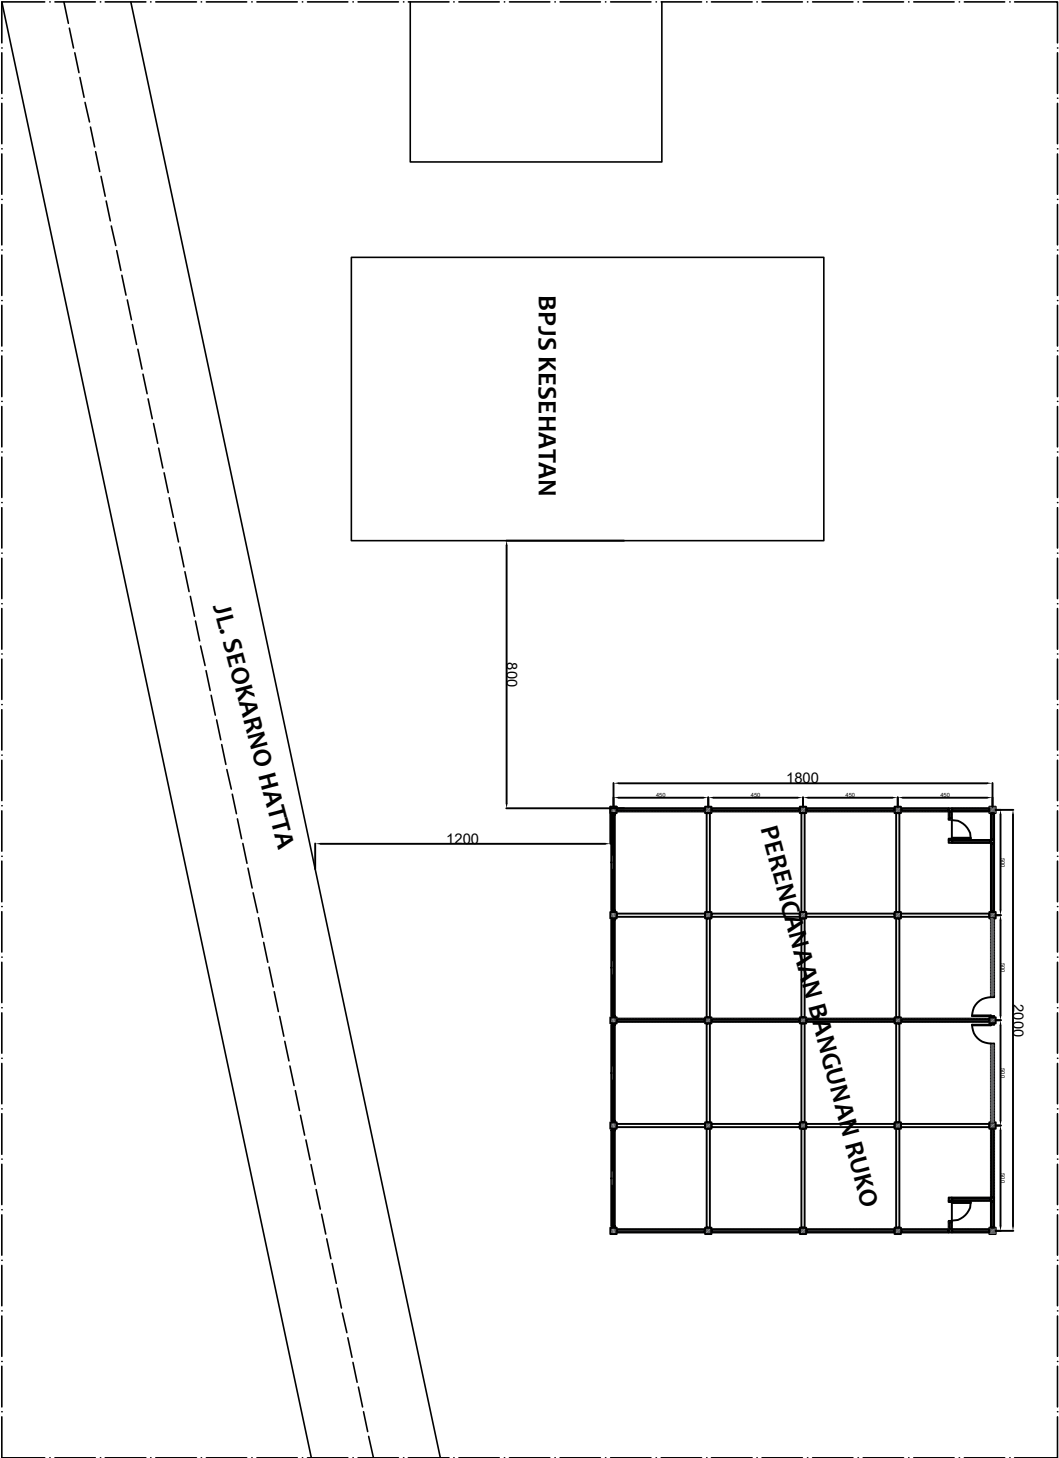

NAMA KEGIATAN			
PERENCANAAN PEMBANGUNAN GEDUNG RUKO			
Pekerjaan			
PERENCANAAN PEMBANGUNAN GEDUNG RUKO SOPIAN SORI			
Lokasi			
JORONG PASAMAN BARU, LINGKUANG AUA, PASAMAN BARAT			
Drafter			
GAMMA ARISKA HARZY, ST			
Judul Gambar	Skala		
SITE PLAN	1 : 100		
Tanggal	Kode Gambar	No.	Jumlah
7 MEI 2025		1	15

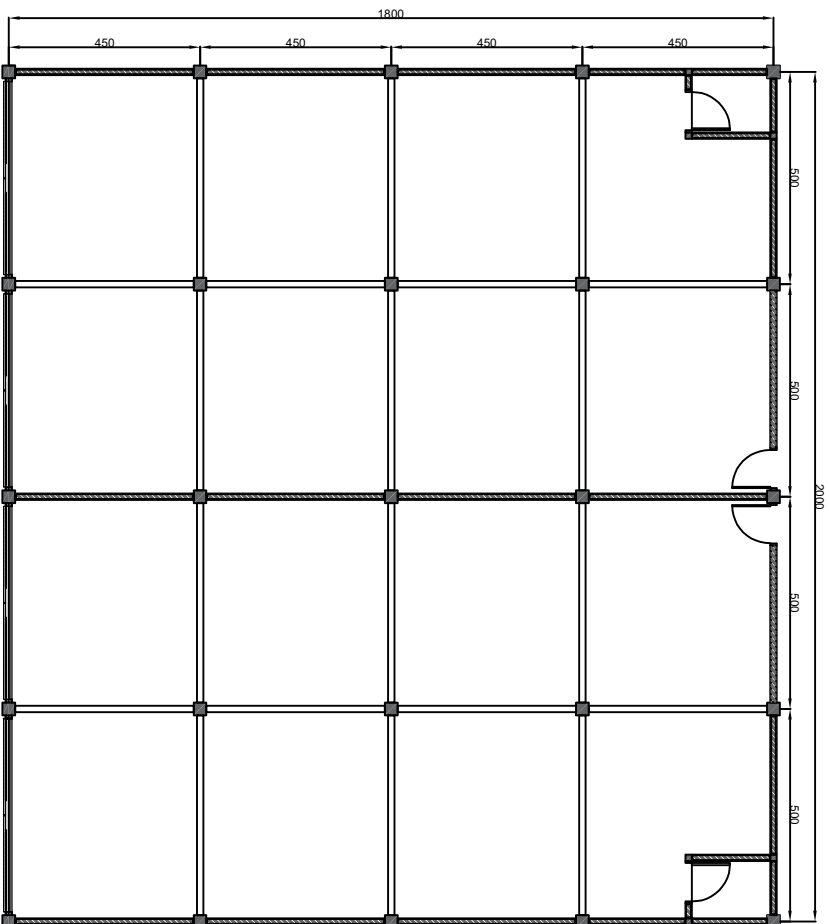

DENAH LAYOUT

Skala 1 : 100

NAMA KEGIATAN

PERENCANAAN PEMBANGUNAN
GEDUNG RUKO

Pekerjaan

PERENCANAAN PEMBANGUNAN GEDUNG
RUKO SOPLAN SORI

Lokasi

JORONG PASAMAN BARU, LINGKUNGAN AUA,
PASAMAN BARAT

Drafter

GAMA ARISKA HARZY, ST


Judul Gambar

Skala

DENAH

1 : 100


Tanggal	Kode Gambar	No.	Jumlah
7 MEI 2025		2	15

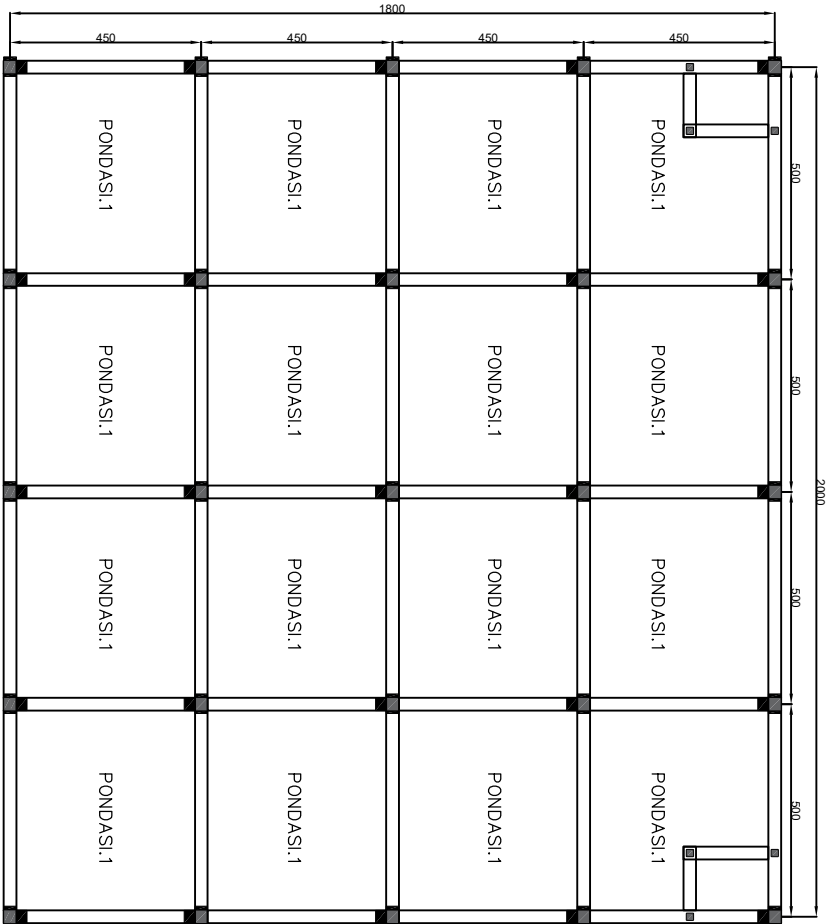

DENAH PONDASI

Skala 1 : 100


NAMA KEGIATAN			
PERENCANAAN PEMBANGUNAN GEDUNG RUKO			
Pekerjaan			
PERENCANAAN PEMBANGUNAN GEDUNG RUKO SOPLAN SORI			
Lokasi			
JORONG PASAMAN BARU, LINGKUNGAN AUA, PASAMAN BARAT			
Drafter			
GAMA ARISKA HARZY, ST			
Judul Gambar		Skala	
DENAH PONDASI		1 : 100	
Tanggal	Kode Gambar	No.	Jumlah
7 MEI 2025		3	15

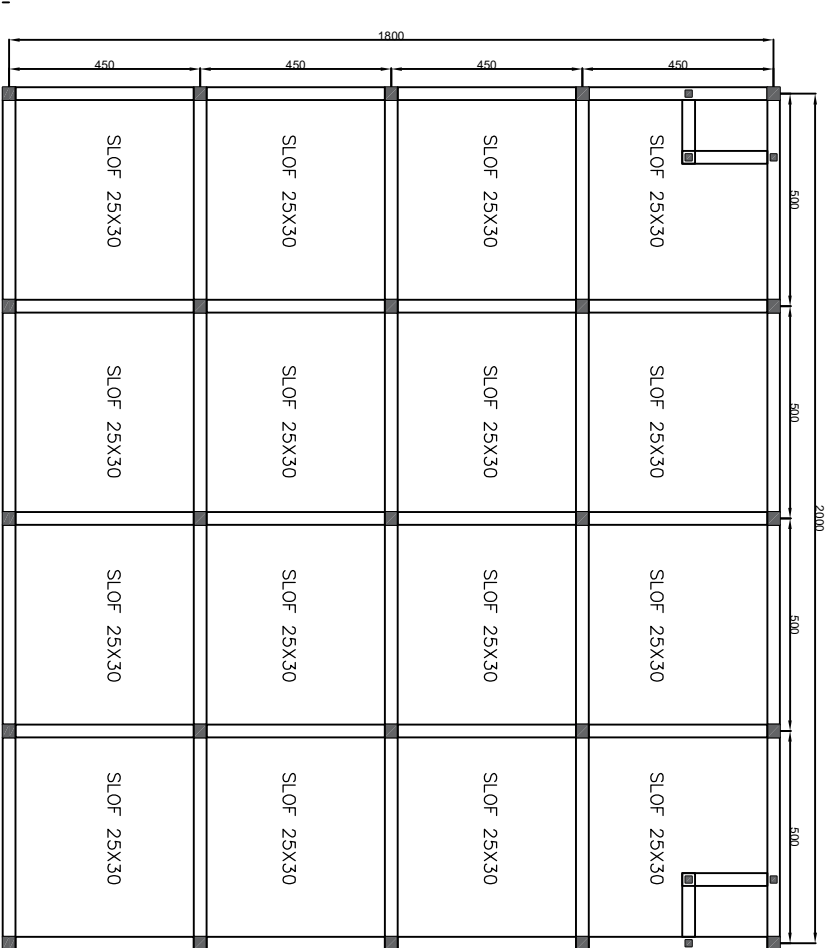


DENAH SLOOF

Skala 1 : 100

NAMA KEGIATAN			
PERENCANAAN PEMBANGUNAN GEDUNG RUKO			
Pekerjaan			
PERENCANAAN PEMBANGUNAN GEDUNG RUKO SOPLAN SORI			
Lokasi			
JORONG PASAMAN BARU, LINGKUNGAN AUA, PASAMAN BARAT			
Drafter			
GAMA ARISKA HARZY, ST		Skala	
Judul Gambar		Skala	
DENAH SLOOF		1 : 100	
Tanggal	Kode Gambar	No.	Jumlah
7 MEI 2025		4	15

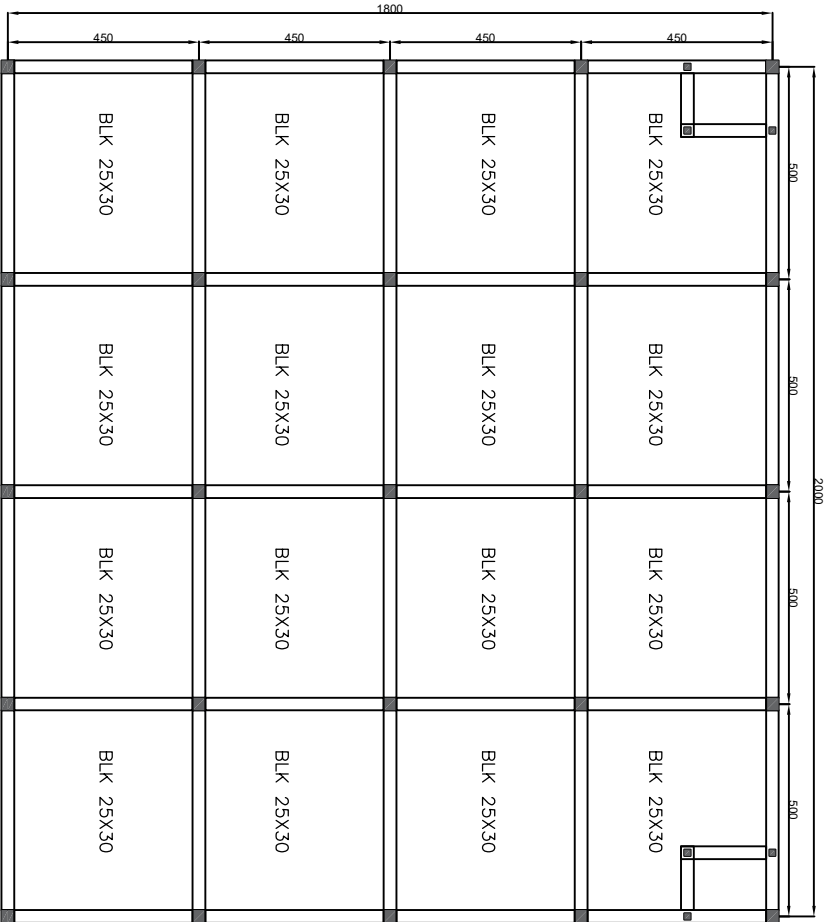

 **DENAH BALOK**
Skala 1 : 100

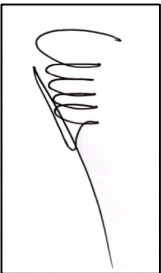NAMA KEGIATAN			
PERENCANAAN PEMBANGUNAN GEDUNG RUKO			
Pekerjaan			
PERENCANAAN PEMBANGUNAN GEDUNG RUKO SOPLAN SORI			
Lokasi			
JORONG PASAMAN BARU, LINGKUNGAN AUA, PASAMAN BARAT			
Drafter			
 GAMA ARISKA HARZY, ST			
Judul Gambar		Skala	
DENAH BALOK		1 : 100	
Tanggal	Kode Gambar	No.	Jumlah
7 MEI 2025		5	15

NAMA KEGIATAN

PERENCANAAN PEMBANGUNAN
GEDUNG RUKO


Pekerjaan

PERENCANAAN PEMBANGUNAN GEDUNG
RUKO SOPLAN SORI

Lokasi

JORONG PASAMAN BARU, LINGKUNGAN AUA,
PASAMAN BARAT

Drafter

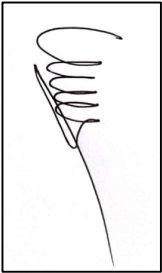

GAMA ARISKA HARZY, ST

Judul Gambar

Skala

DENAH KOLOM

1 : 100

Tanggal Kode Gambar No. Jumlah

7 MEI 2025


6

15



DENAH KOLOM

Skala 1 : 100

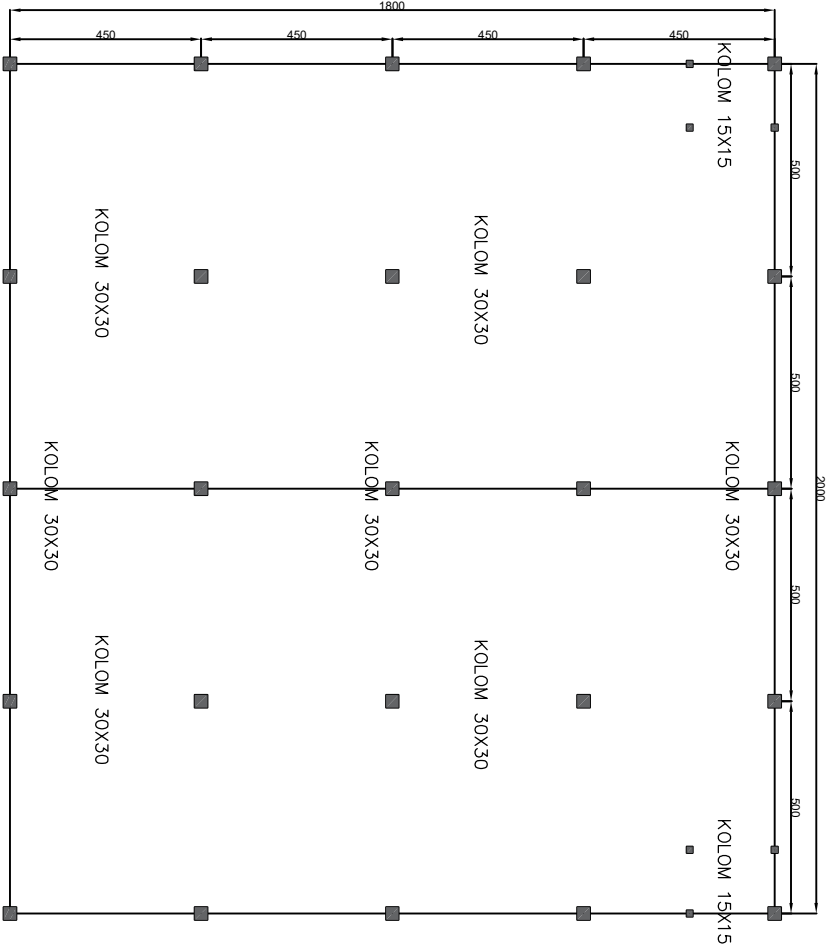

NAMA KEGIATAN

PERENCANAAN PEMBANGUNAN
GEDUNG RUKO


Pekerjaan

Lokasi

PERENCANAAN PEMBANGUNAN
GEDUNG RUKO SOPIAN SORI

JORONG PASAMAN BARU LINGKUANG
AUA, PASAMAN BARAT

Drafter

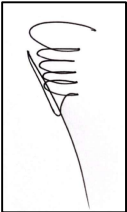

GAMARA ARISKA HARZV, ST

Judul Gambar

Skala

DETAIL

1 : 100

Tanggal	Kode Gambar	No.	Jumlah
7 MEI 2025		7	15







TABEL PENULANGAN

Skala 1 : 100

TABEL PENULANGAN


DETAIL PONDASI

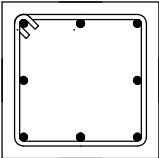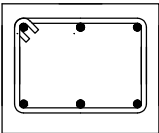GEOMETRI SLOOF DAN KOLOM	KOLOM	SLOOF & BLK	
	30 X 30	25 X 30	
			
	DIMENSI	30/30	25/30
	TUL. ATAS	3 D -16	2 D -16
TUL. TENGAH	2 D -16	2 D -16	
TUL. BAWAH	3 D -16	2 D -16	
SENGKANG	ø10-20 CM	ø10-20 CM	

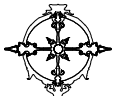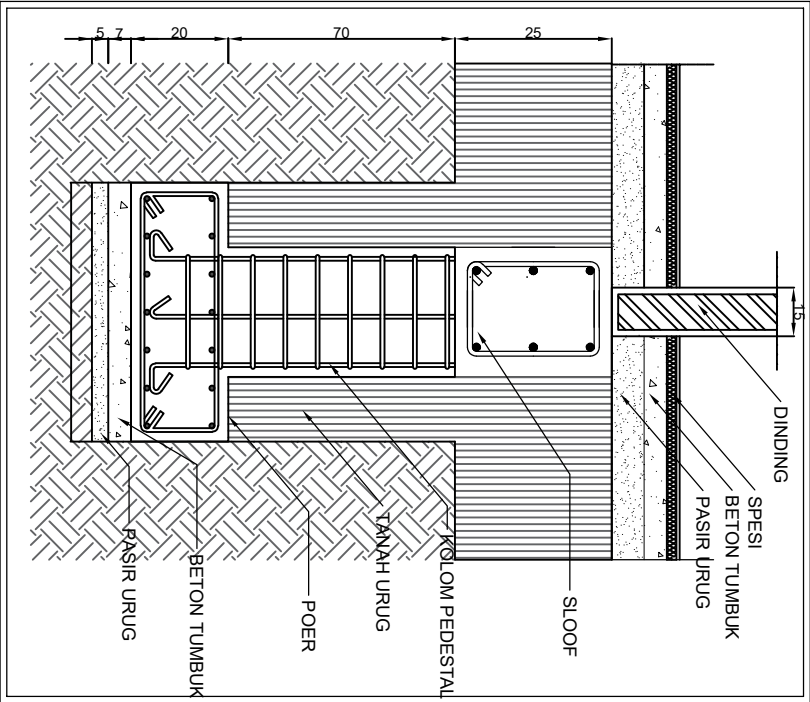


DETAIL PONDASI

25 UNIT

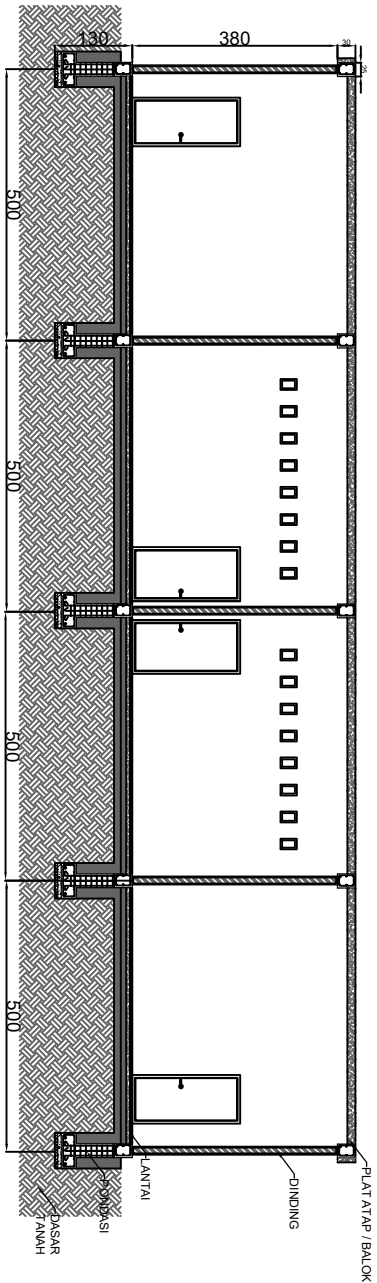

POTONGAN MEMANJANG

Skala 1 : 100

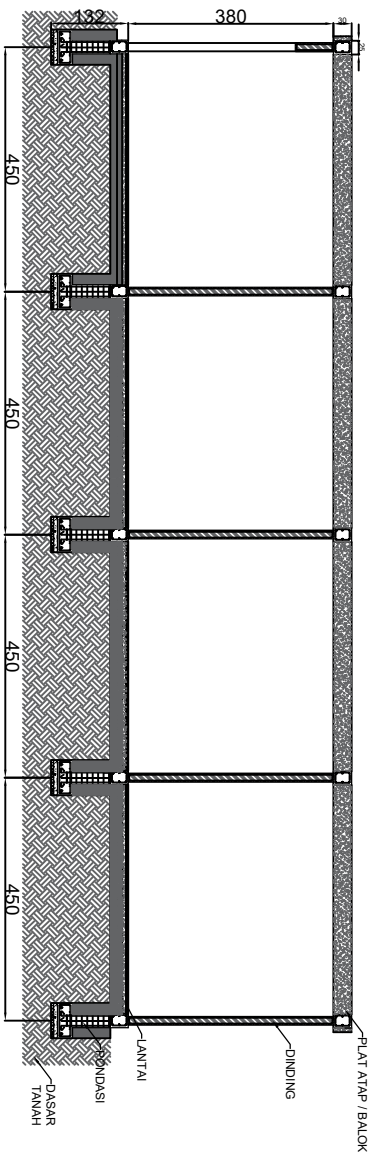

POTONGAN MELINTANG

Skala 1 : 100

NAMA KEGIATAN

PERENCANAAN PEMBANGUNAN
GEDUNG RUKO

Pekerjaan

PERENCANAAN PEMBANGUNAN
GEDUNG RUKO SOPIAN SORI

Lokasi

JORONG PASAMAN BARU LINGKUANG
AUA, PASAMAN BARAT

Drafter

GAMA ARISKA HARZY, ST

Judul Gambar

Skala

POTONGAN

1 : 100

Tanggal

Kode Gambar


No.

Jumlah

7 MEI 2025


8

15

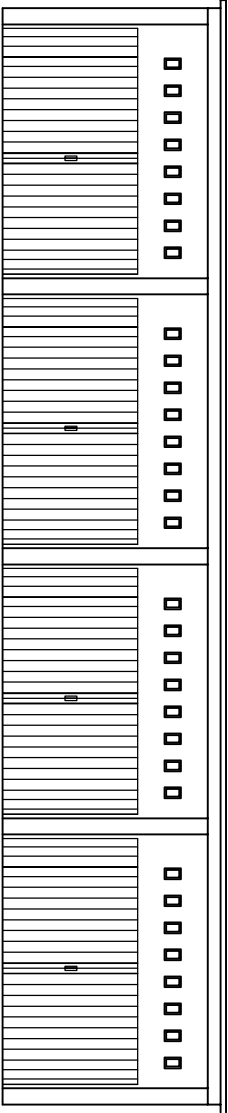

TAMPAK DEPAN


Skala 1 : 100

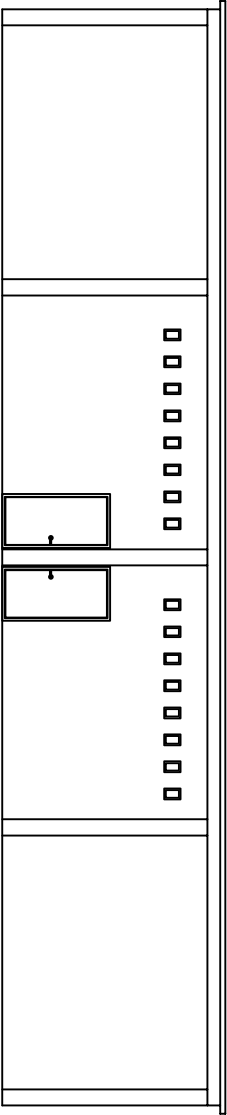

TAMPAK BELAKANG


Skala 1 : 100

NAMA KEGIATAN			
PERENCANAAN PEMBANGUNAN GEDUNG RUKO			
Pekerjaan			
PERENCANAAN PEMBANGUNAN GEDUNG RUKO SOPIAN SORI			
Lokasi			
JORONG PASAMAN BARU LINGKUNGAN AUA, PASAMAN BARAT			
Drafter			
GAMA ARISKA HARZY, ST			
Judul Gambar		Skala	
TAMPAK		1 : 100	
Tanggal	Kode Gambar	No.	Jumlah
7 MEI 2025		9	15

 


TAMPAK S. KANAN


Skala 1 : 100

 

TAMPAK S. KIRI

Skala 1 : 100

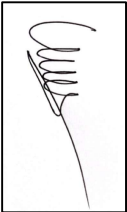NAMA KEGIATAN			
PERENCANAAN PEMBANGUNAN GEDUNG RUKO			
Pekerjaan			
PERENCANAAN PEMBANGUNAN GEDUNG RUKO SOPIAN SORI			
Lokasi			
JORONG PASAMAN BARU LINGKUANG AUA, PASAMAN BARAT			
Drafter			
			
GAMA ARISKA HARZY, ST			
Judul Gambar	Skala		
TAMPAK	1 : 100		
Tanggal	Kode Gambar	No.	Jumlah
7 MEI 2025		10	15

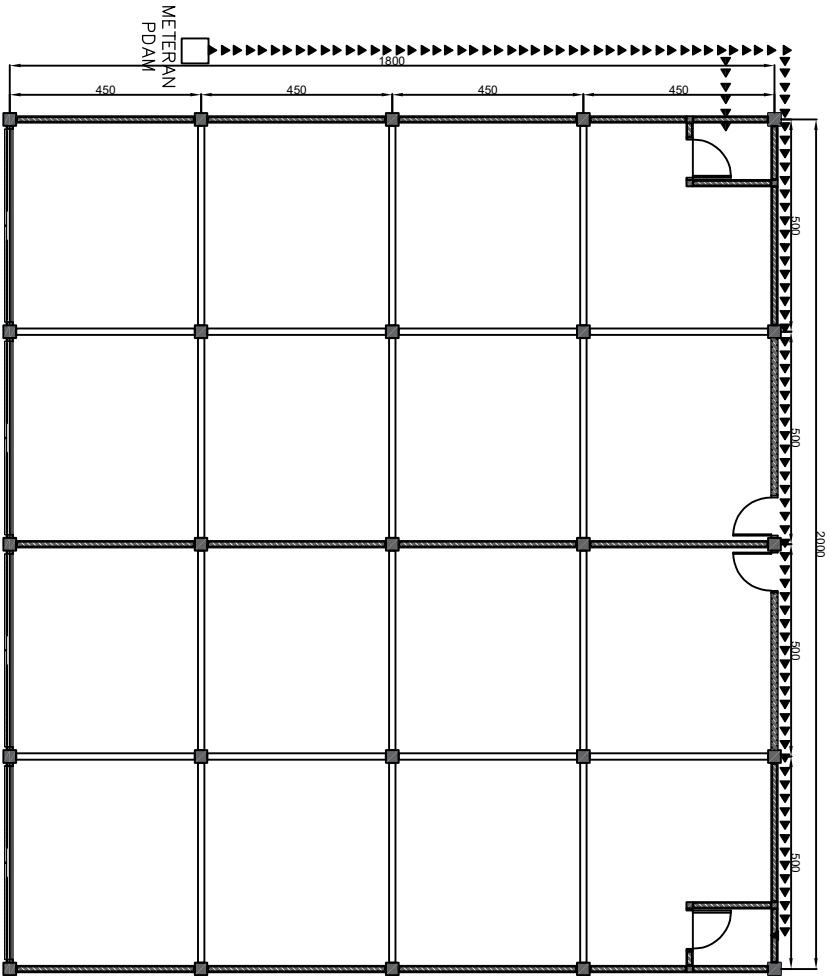

 **DENAH INSTALASI AIR BERSIH**
Skala 1 : 100

NAMA KEGIATAN

PERENCANAAN PEMBANGUNAN
GEDUNG RUKO


Pekerjaan

PERENCANAAN PEMBANGUNAN GEDUNG
RUKO SOPAN SORI

Lokasi

JORONG PASAMAN BARU, LINGKUNGAN ALA,
PASAMAN BARAT

Drafter

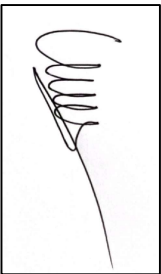

GAMA ARISKA HARZY, ST

Judul Gambar

Skala

DENAH INSTALASI
AIR BERSIH

1 : 100

Tanggal

Kode Gambar

No.

Jumlah


7 MEI 2025


12

15

DENAH INSTALASI AIR KOTOR

Skala 1 : 100

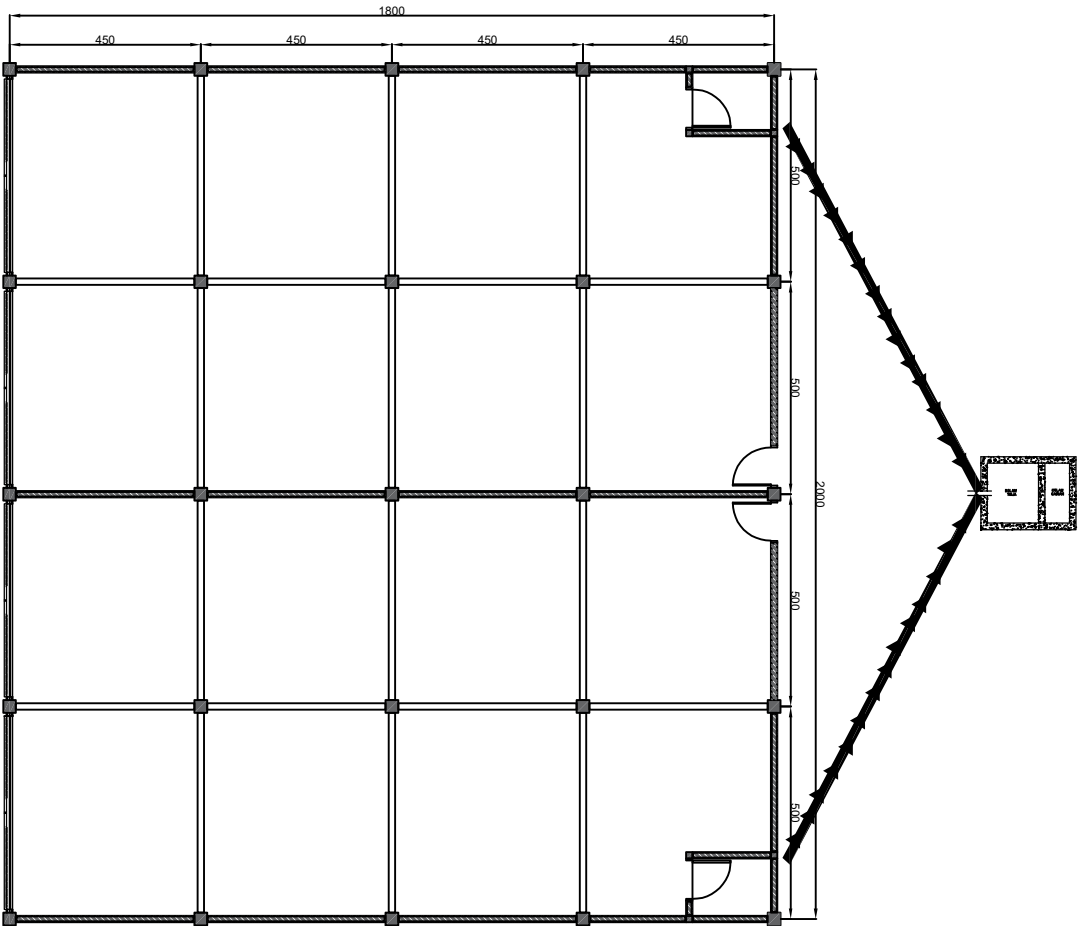

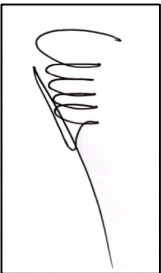NAMA KEGIATAN			
PERENCANAAN PEMBANGUNAN GEDUNG RUKO			
Pekerjaan			
PERENCANAAN PEMBANGUNAN GEDUNG RUKO SOPLAN SORI			
Lokasi			
JORONG PASAMAN BARU, LINGKUNGAN AUA, PASAMAN BARAT			
Drafter			
			
GAMA ARISKA HARZY, ST			
Judul Gambar	Skala		
DENAH INSTALASI AIR KOTOR	1 : 100		
Tanggal	Kode Gambar	No.	Jumlah
7 MEI 2025		13	15

NAMA KEGIATAN

PERENCANAAN PEMBANGUNAN
GEDUNG RUKO


Pekerjaan

PERENCANAAN PEMBANGUNAN GEDUNG
RUKO SOPLAN SORI

Lokasi

JORONG PASAMAN BARU, LINGKUNGAN AUA,
PASAMAN BARAT

Drafter

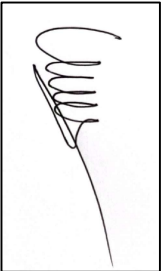

GAMA ARISKA HARZY, ST

Judul Gambar

Skala

DENAH INSTALASI
LISTRIK

1 : 100

Tanggal Kode Gambar No. Jumlah

7 MEI 2025


14

15




DENAH INSTALASI LISTRIK


Skala 1 : 100

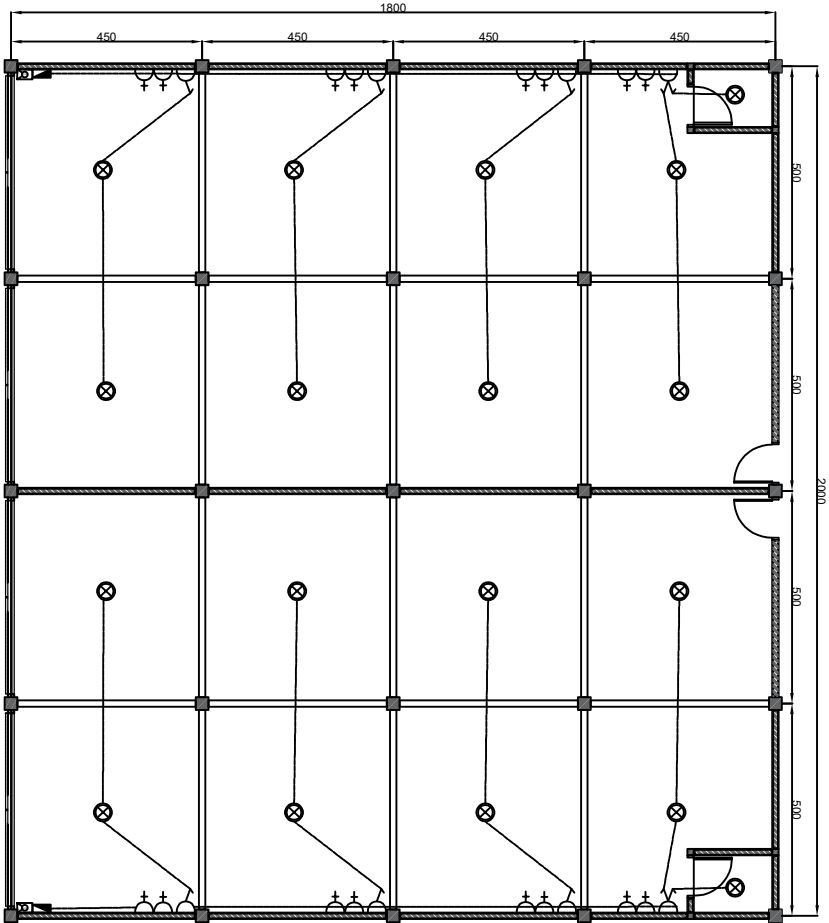

KETERANGAN INSTALASI LISTRIK			
NO	Simbol	Unit	REMARKS
1		18	LAMPU DOWNLIGHT PLANO 18W
2		6	SAKUP TANGGAL
3		16	STOP KONTAK GEMUK
4		2	SAKUP GEMUK
5		2	RELOKETERLAMU
6		2	KONTAK MUKA

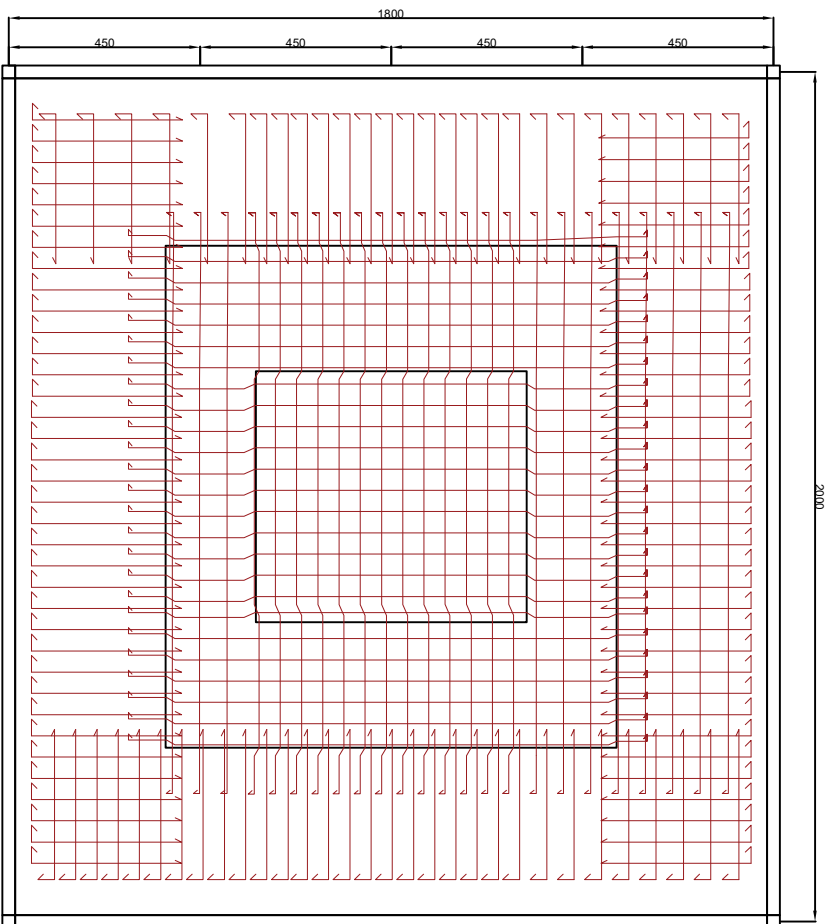

 **DENAH DACK BETON**
Skala 1 : 100

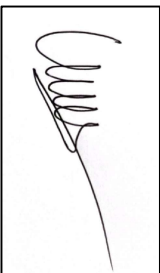NAMA KEGIATAN			
PERENCANAAN PEMBANGUNAN GEDUNG RUKO			
Pekerjaan			
PERENCANAAN PEMBANGUNAN GEDUNG RUKO SOPIAN SORI			
Lokasi			
JORONG PASAMAN BARU, LINGKUANG AUA, PASAMAN BARAT			
Drafter			
			
GAMA ARISKA HARZY, ST		Skala	
Judul Gambar		1 : 100	
DENAH DACK BETON			
Tanggal	Kode Gambar	No.	Jumlah
7 MEI 2025		15	15